
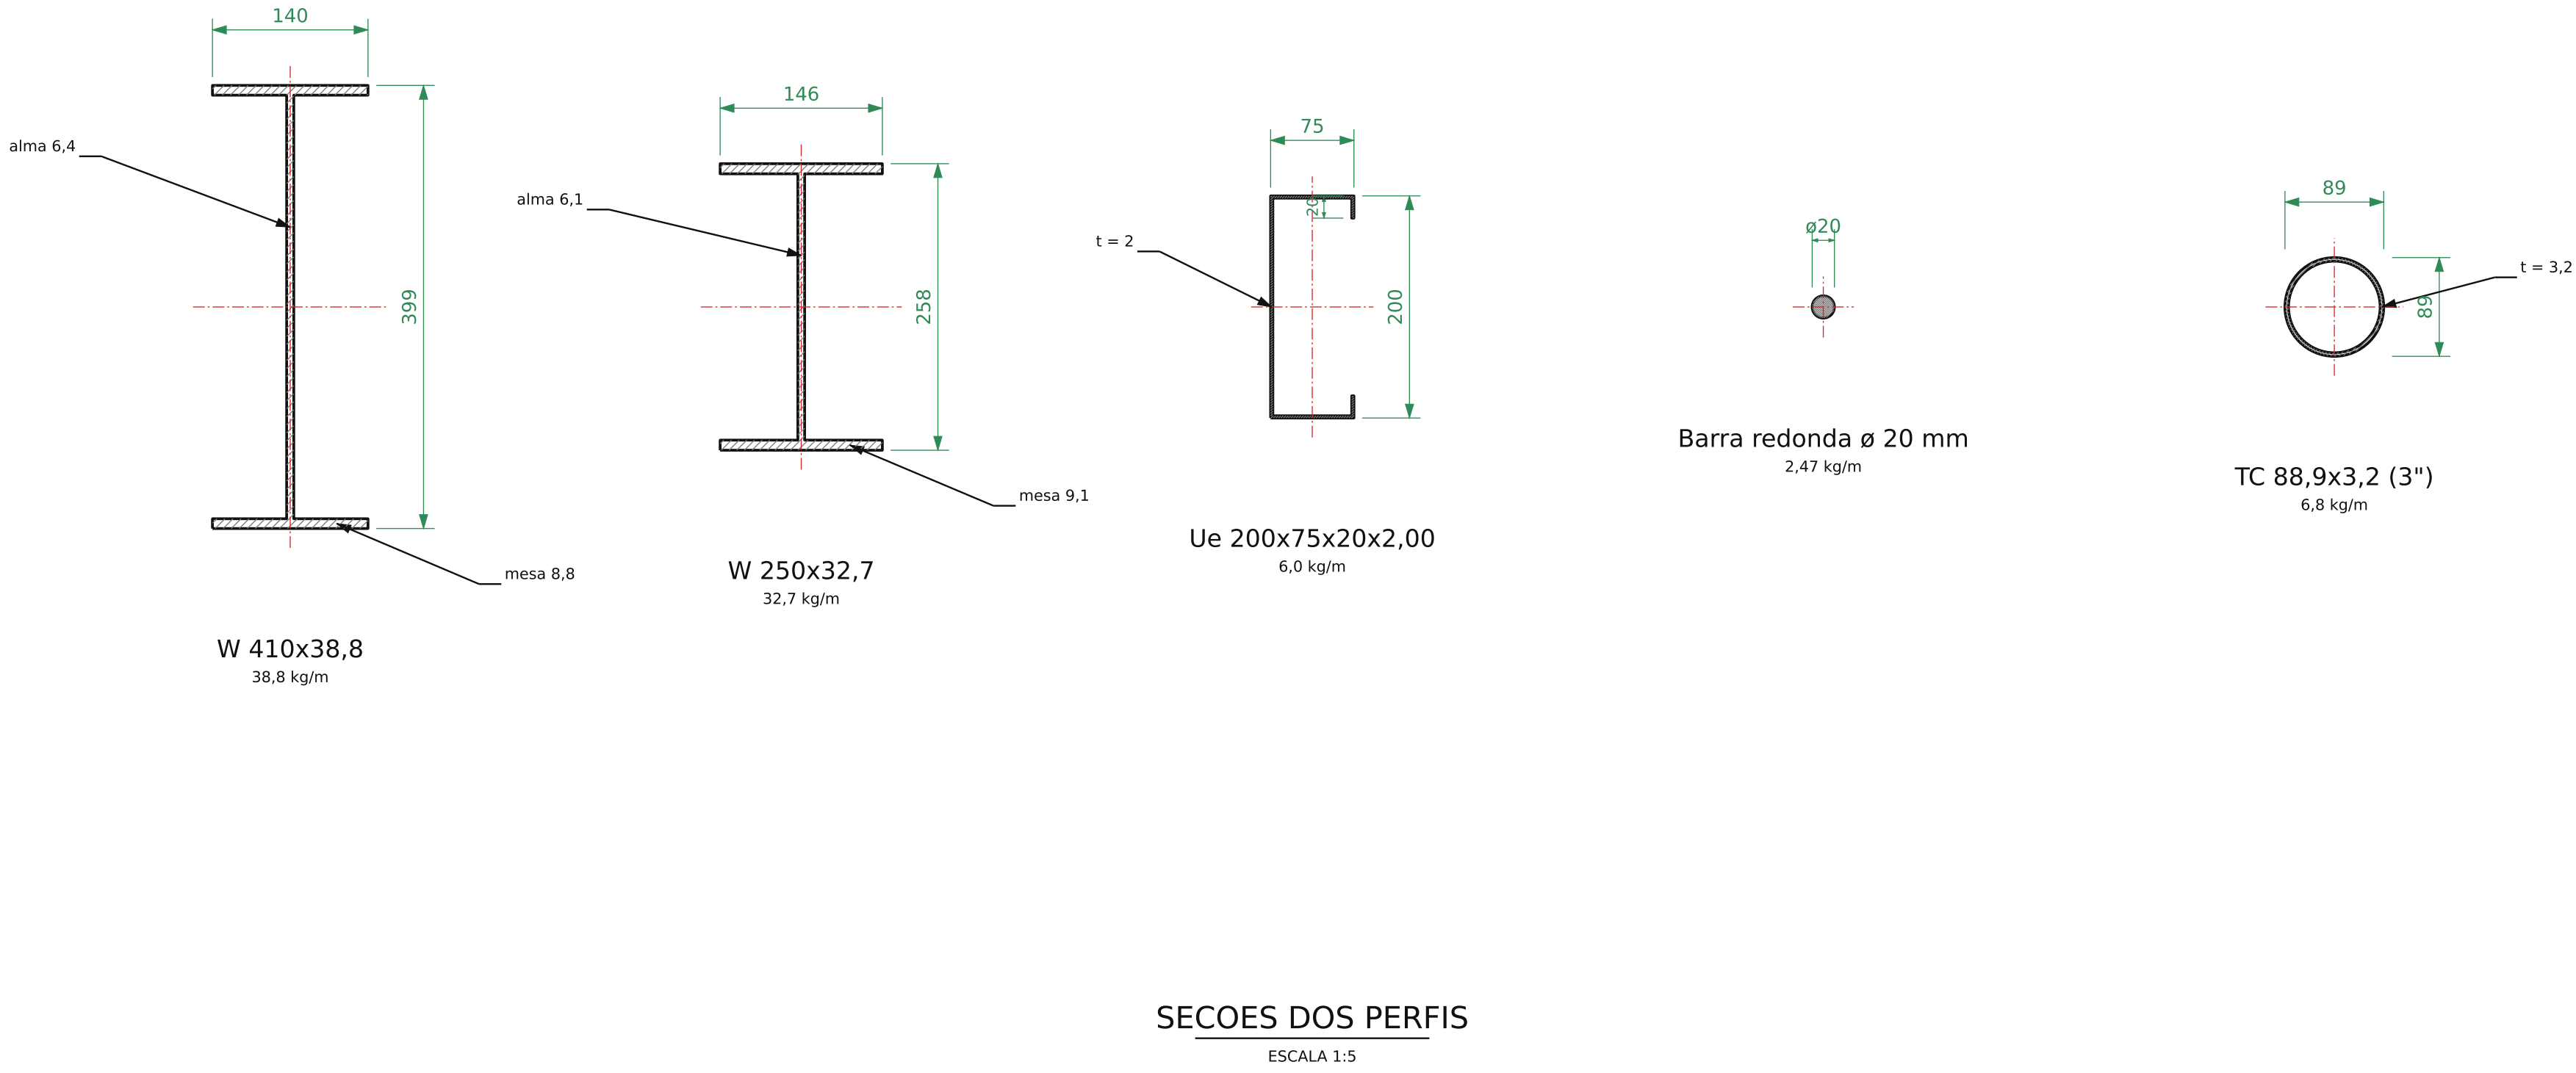


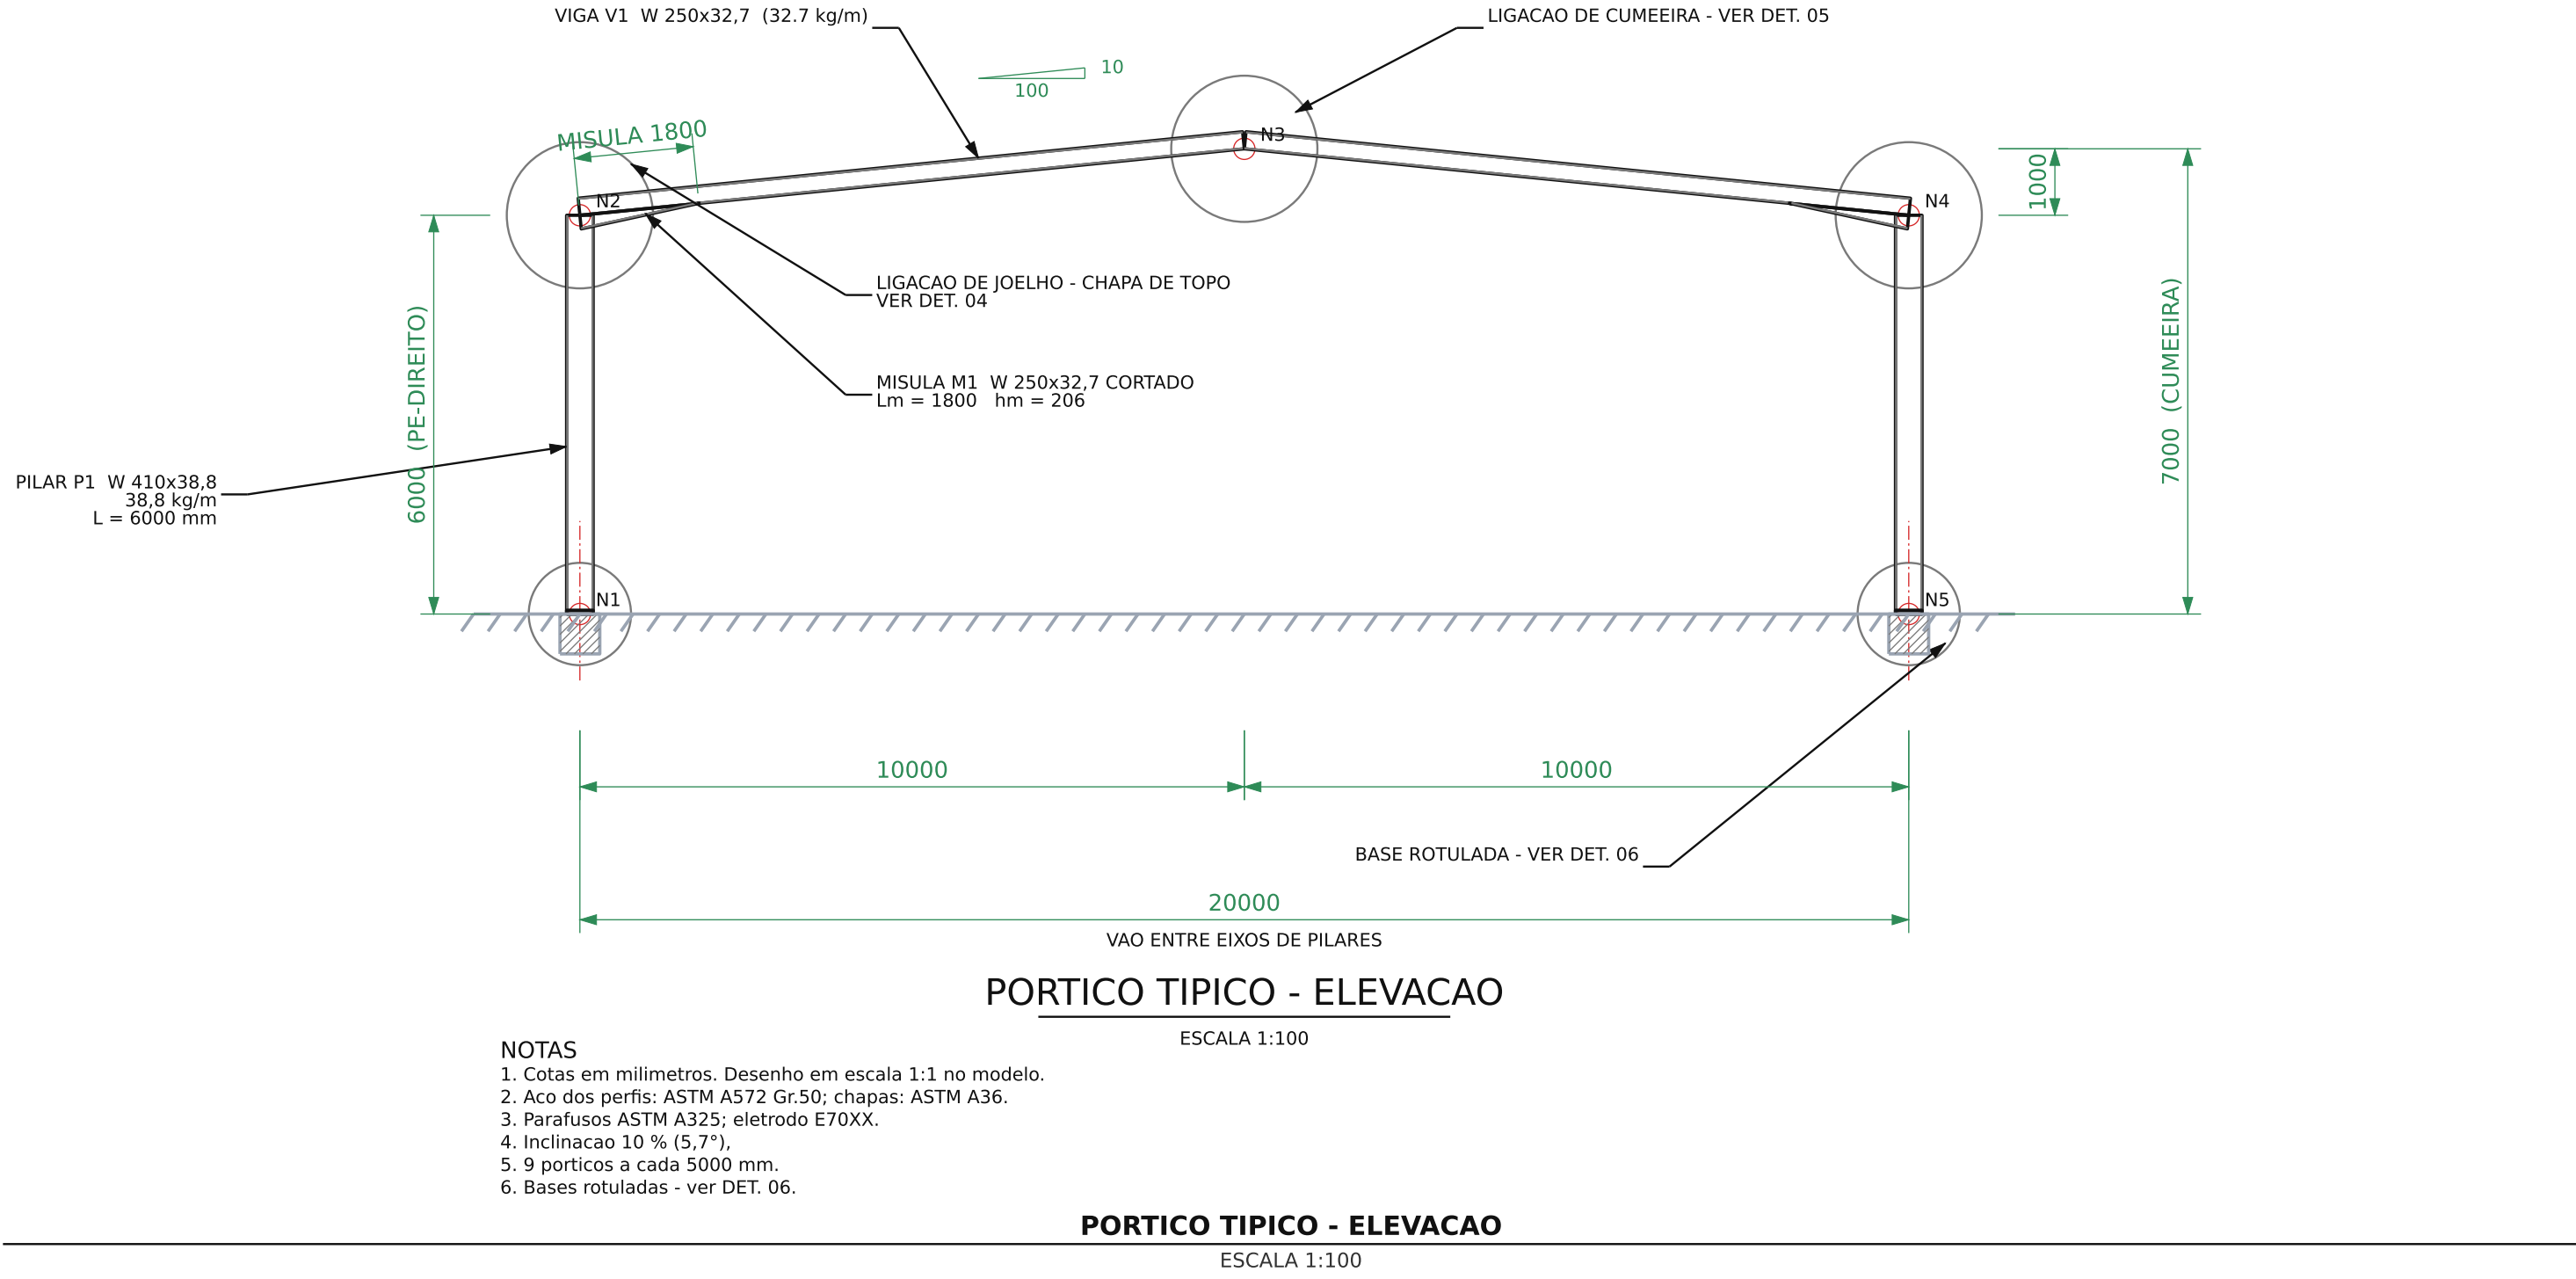

OBRA Galpao Exemplo		
CLIENTE Cliente Exemplo Ltda		
TÍTULO DO DESENHO Pórtico típico e seções dos perfis		
Portico tipico - elevacao - Secoes dos perfis		
RESPONSÁVEL TÉCNICO Eng. Responsavel Tecnico CREA nº _____ — ART nº _____	ESCALA indicadas DATA 11/09/2026	PRANCHA 01/06 REV. 00
Desenho gerado automaticamente. Deve ser conferido e assinado por engenheiro habilitado, com ART no CREA, antes da fabricação.		