



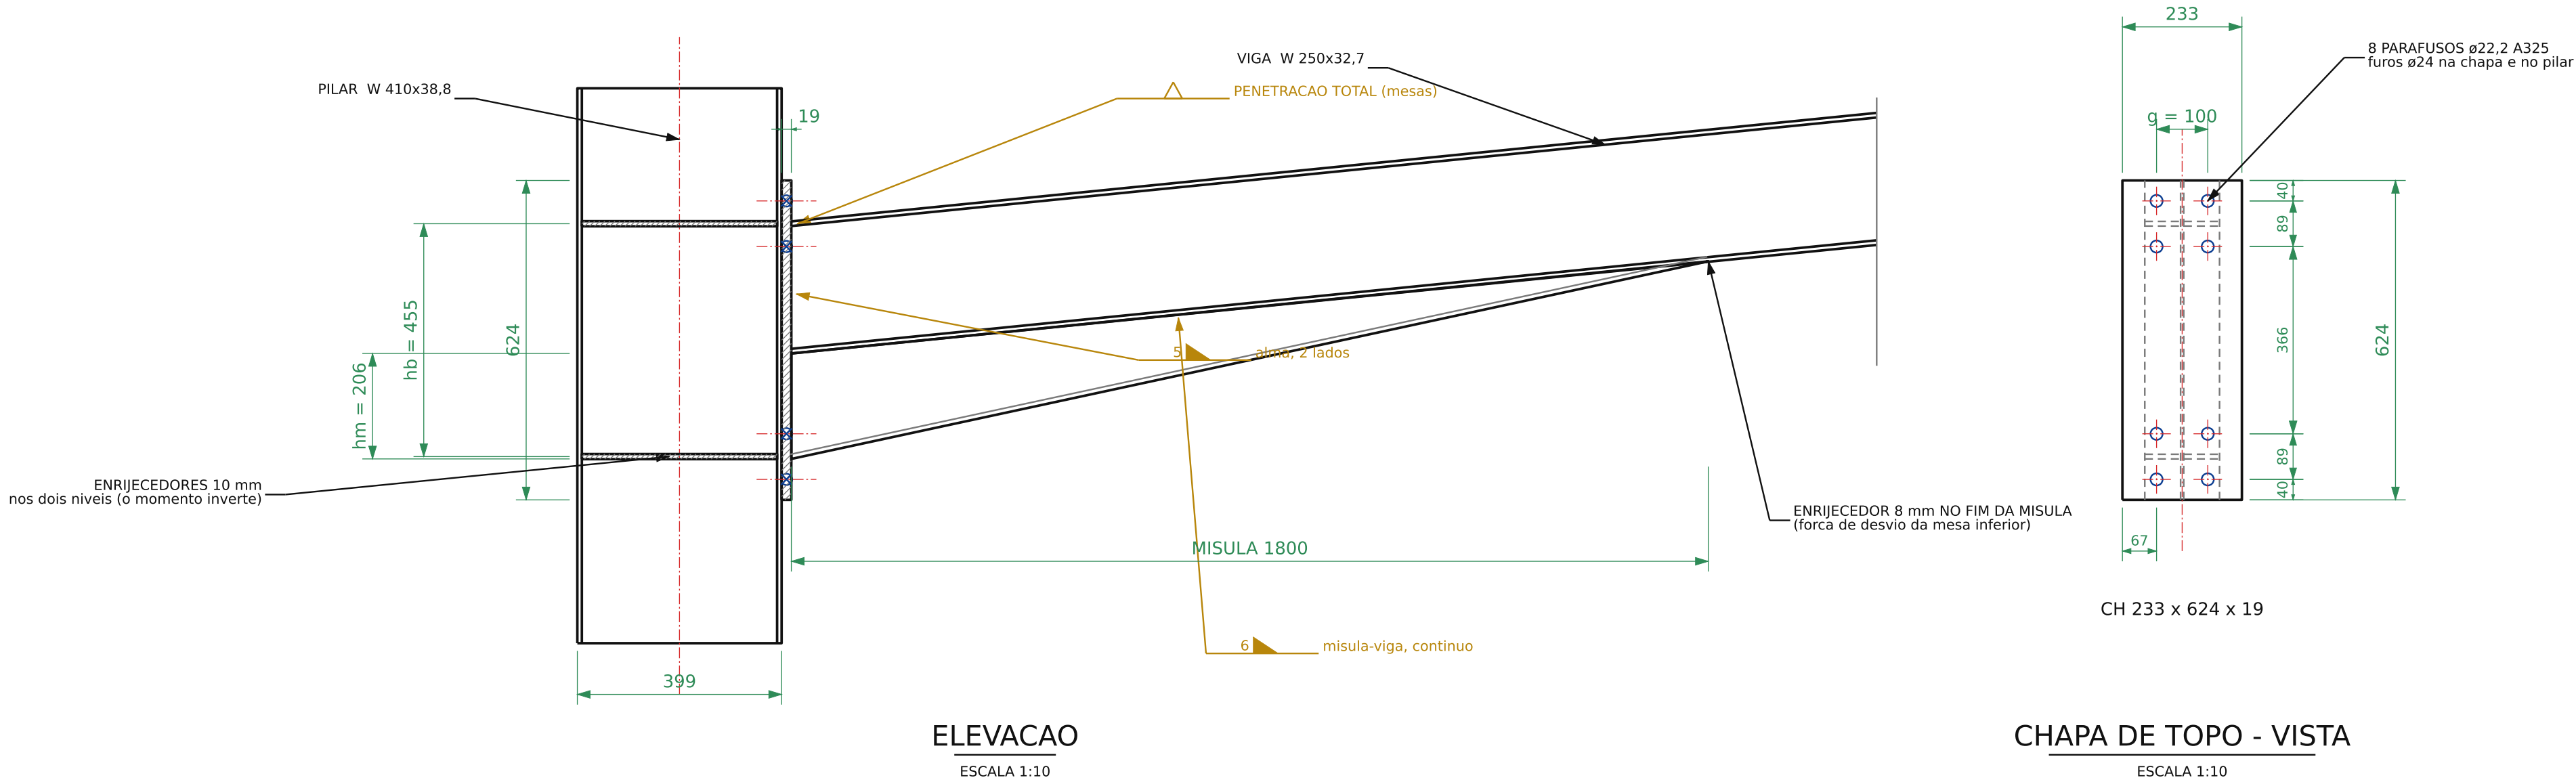

- NOTAS
- Cotas em milímetros.
 - Chapa de topo estendida 233 x 624 x 19 mm.
 - 8 parafusos ø22,2 A325, furos ø24 mm.
 - Soldas das mesas com penetração total; alma com filete 5 mm nos dois lados.
 - Enrijecedores do pilar no nível das duas mesas (o momento inverte de sinal).
 - Faces de contato sem pintura; parafusos protendidos.

LIGACAO VIGA-PILAR (JOELHO)

ESCALA 1:10

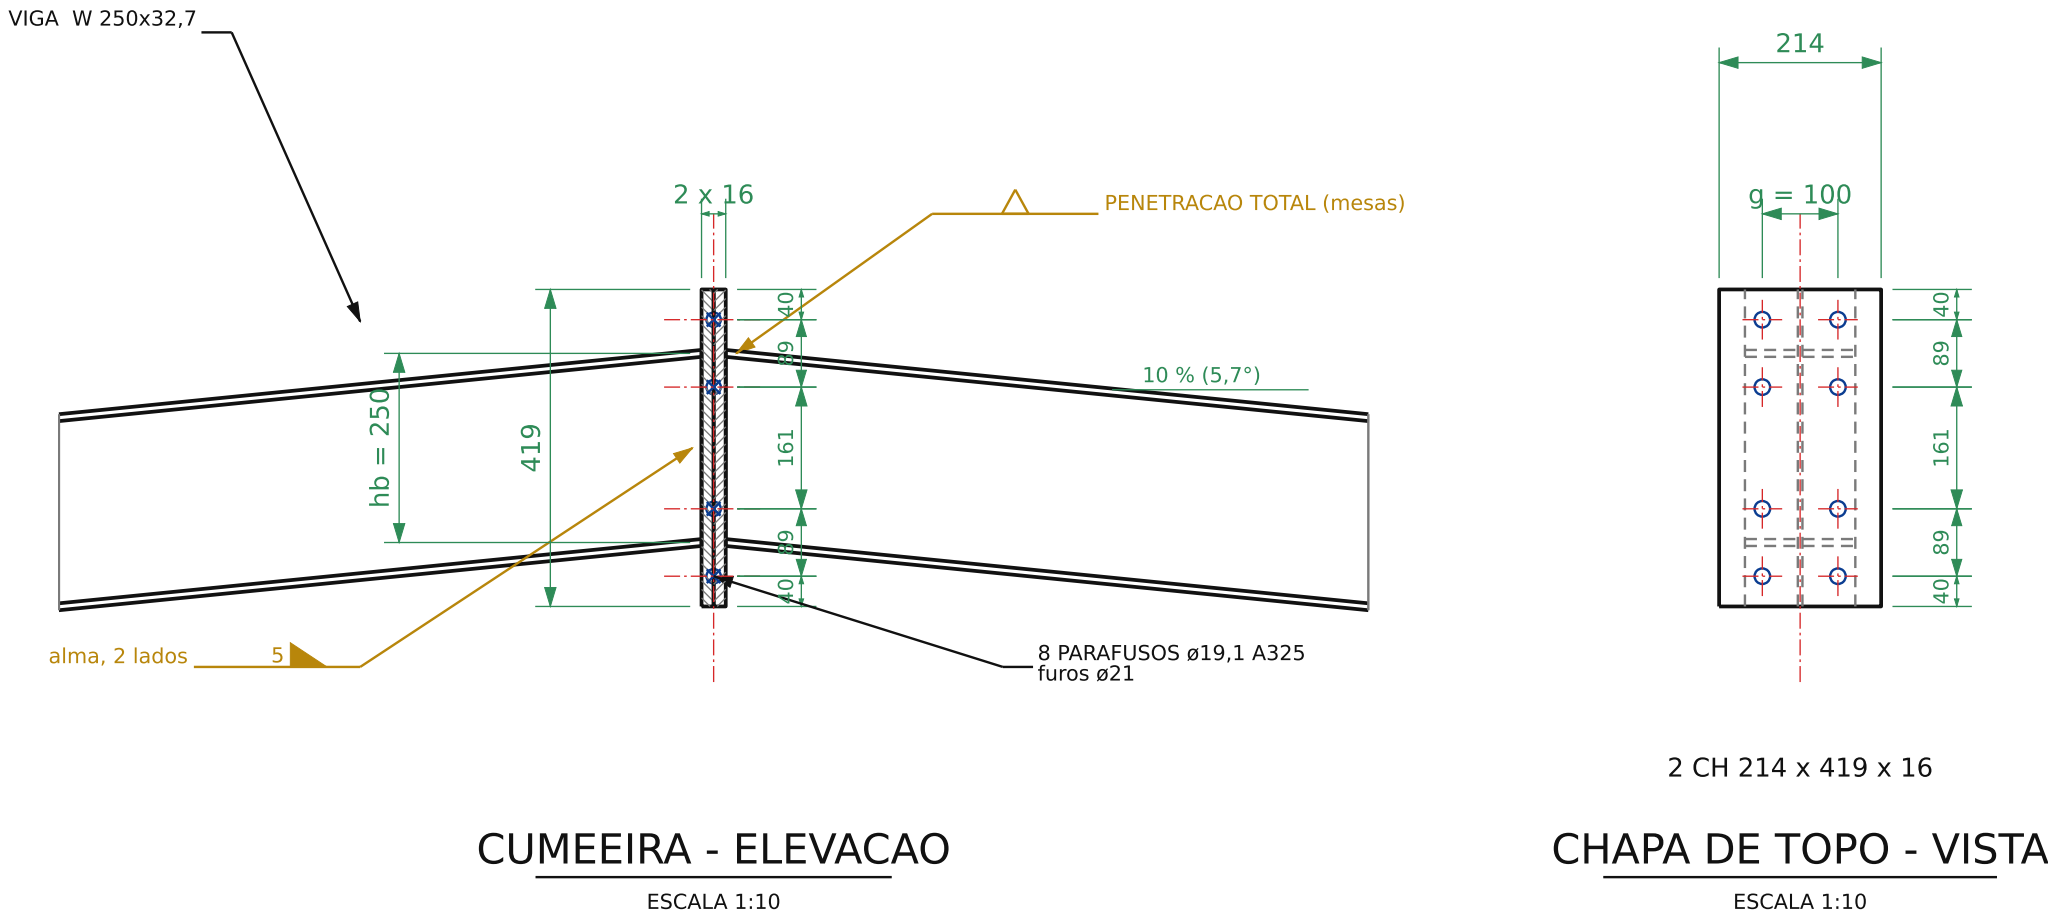

- NOTAS
- Cotas em milímetros.
 - Chapas cortadas no angulo do telhado; faces de contato planas.
 - 8 parafusos ø19,1 A325.
 - Mao-francesa obrigatória na terça de cumeeira, dos dois lados (Cap. 14.1.4).

LIGACAO DE CUMEEIRA

ESCALA 1:10

OBRA		
Galpao Exemplo		
CLIENTE		
Cliente Exemplo Ltda		
TÍTULO DO DESENHO		
Ligações do pórtico — joelho e cumeeira		
Ligacao viga-pilar (joelho) · Ligacao de cumeeira		
RESPONSÁVEL TÉCNICO	ESCALA	PRANCHA
Eng. Responsavel Técnico	1:10	03/06
CREA nº _____ — ART nº _____	DATA 11/09/2026	REV. 00
Desenho gerado automaticamente. Deve ser conferido e assinado por engenheiro habilitado, com ART no CREA, antes da fabricação.		