



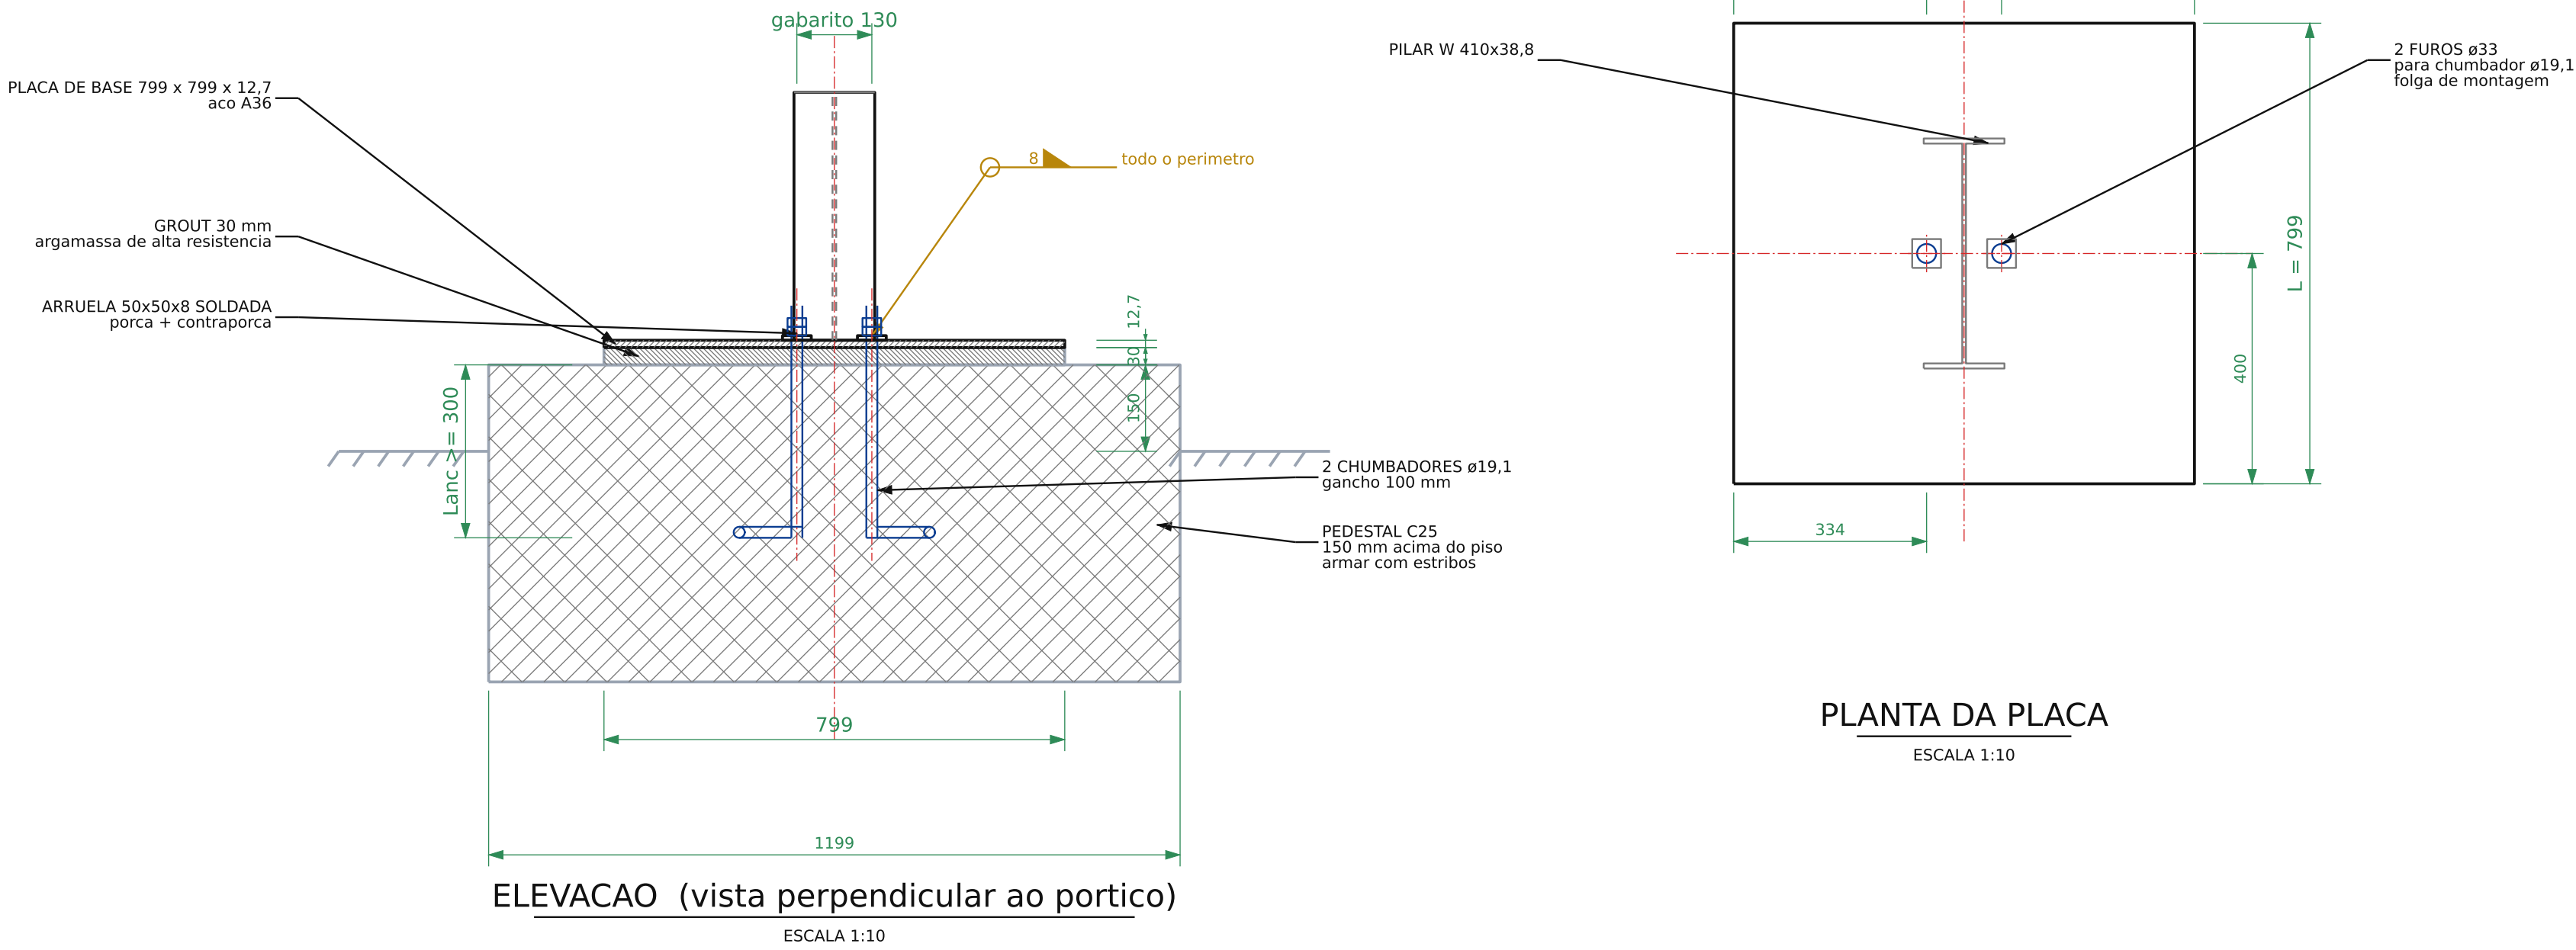

- NOTAS
1. Cotas em milímetros.
  2. Base rotulada; chumbadores no eixo do pilar, sem braco de alavanca.
  3. Placa 799 x 799 x 12,7 mm em A36; grout de 30 mm.
  4. Chumbadores ø19,1, ancoragem >= 300 mm mais gancho de 100 mm.
  5. Furos ø33 mm na placa (folga de montagem) com arruela 50x50x8 soldada apos o prumo.
  6. Nivelar a placa com porcas antes do grout; conferir prumo e cota de topo.

BASE DO PILAR  
ESCALA 1:10

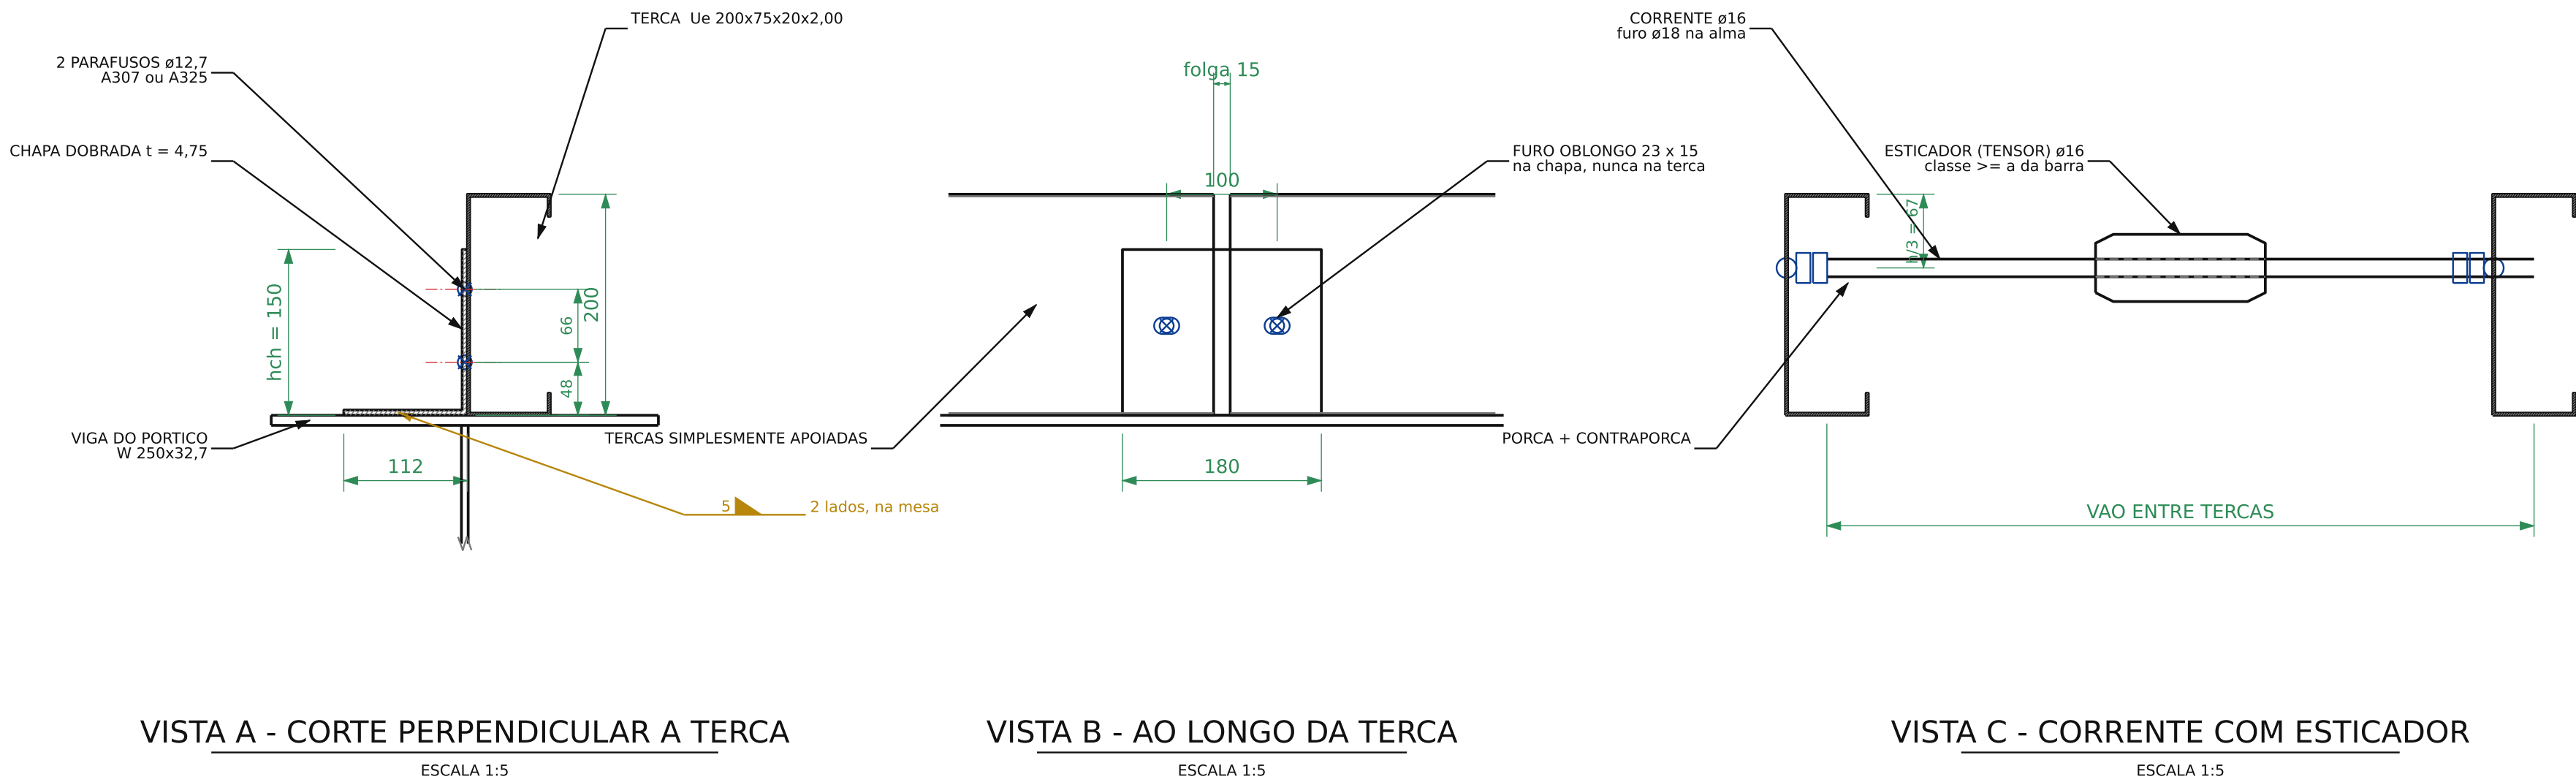

- NOTAS
1. Cotas em milímetros.
  2. Chapa de terça t = 4,75 mm, altura 150 mm (0,7 a 0,8 da altura da terça).
  3. Solda de filete 5 mm nos dois lados, na mesa da viga.
  4. Furos oblongos apenas na chapa; na terça, furo redondo ø15 mm.
  5. Nunca soldar a terça na viga em campo (queima a galvanizacao).
  6. Corrente ø16 no terço superior da alma, sempre com esticador.

APOIO DE TERÇA E CORRENTE  
ESCALA 1:5

|   |                                               |                                    |
|---|-----------------------------------------------|------------------------------------|
| OBRA<br><b>Galpao Exemplo</b>                                                                                                  |                                               |                                    |
| CLIENTE<br>Cliente Exemplo Ltda                                                                                                |                                               |                                    |
| TÍTULO DO DESENHO<br><b>Base do pilar e apoio de terça</b><br>Base do pilar - Apoio de terça e corrente                        |                                               |                                    |
| RESPONSÁVEL TÉCNICO<br><b>Eng. Responsavel Tecnico</b><br>CREA nº _____ — ART nº _____                                         | ESCALA<br><b>indicadas</b><br>DATA 11/09/2026 | PRANCHA<br><b>04/06</b><br>REV. 00 |
| Desenho gerado automaticamente. Deve ser conferido e assinado por engenheiro habilitado, com ART no CREA, antes da fabricação. |                                               |                                    |