




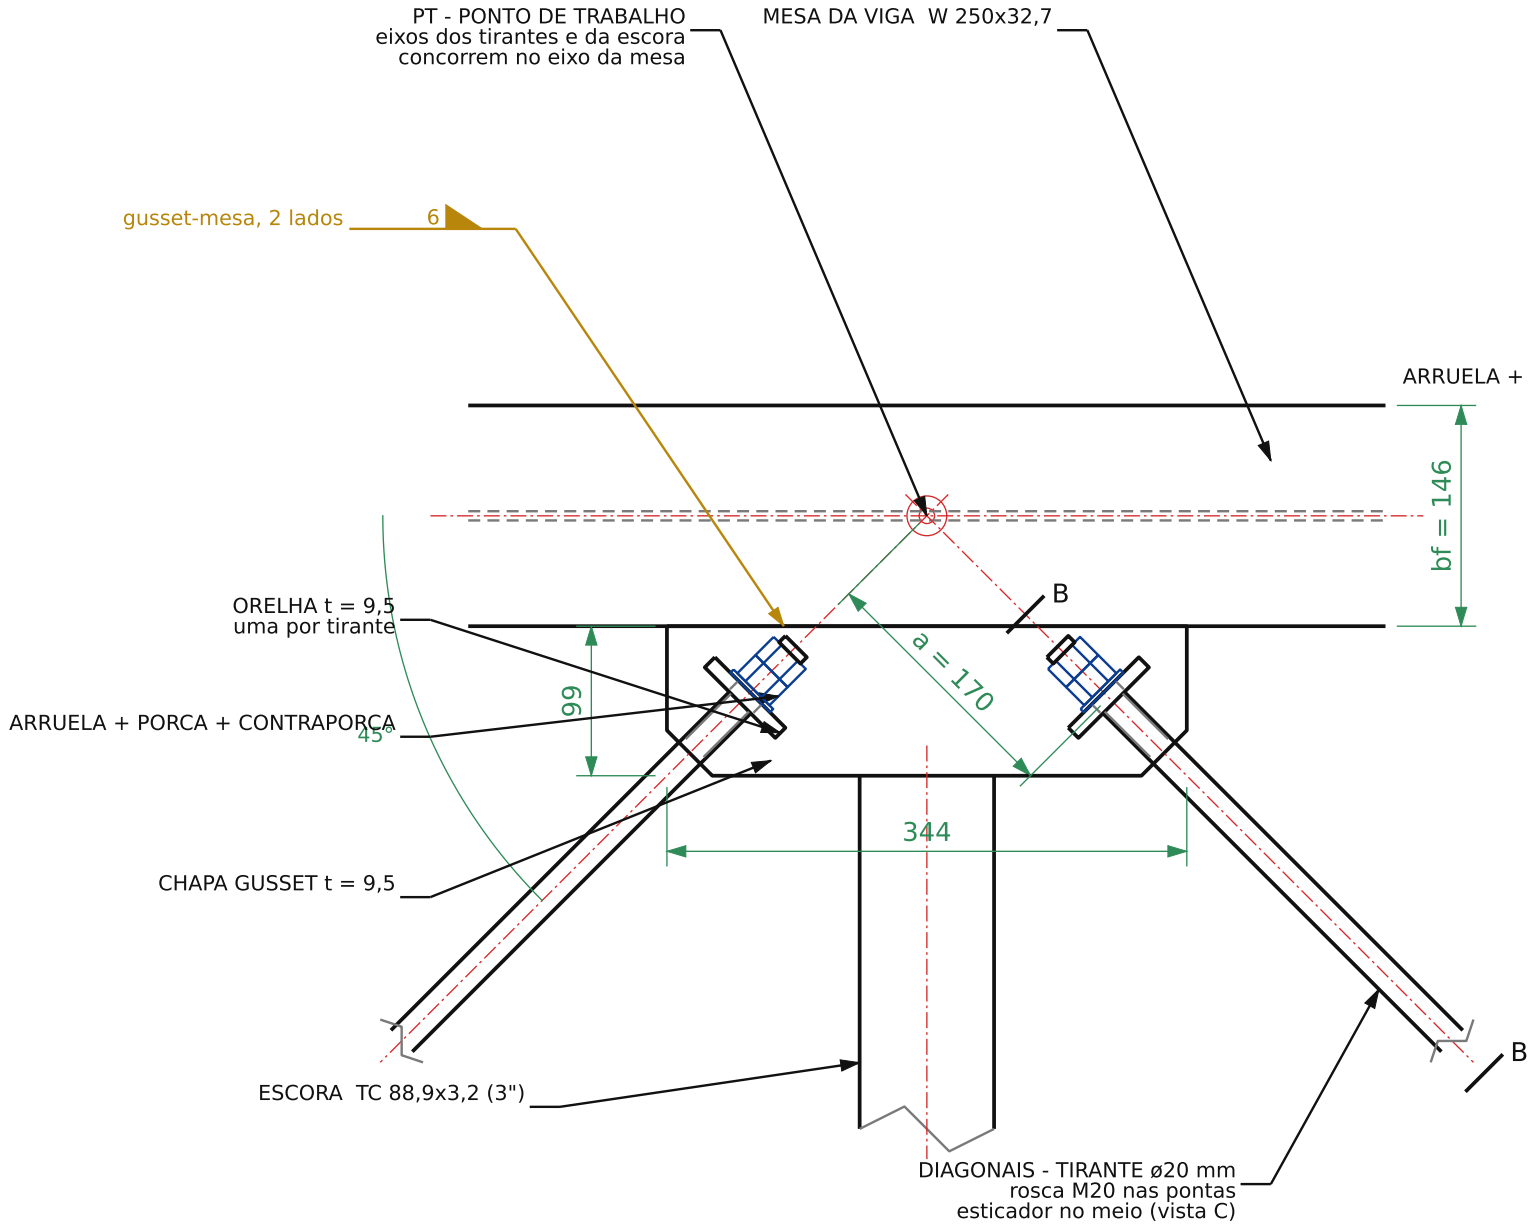

PLANTA DO NO - TIRANTES
ESCALA 1:5

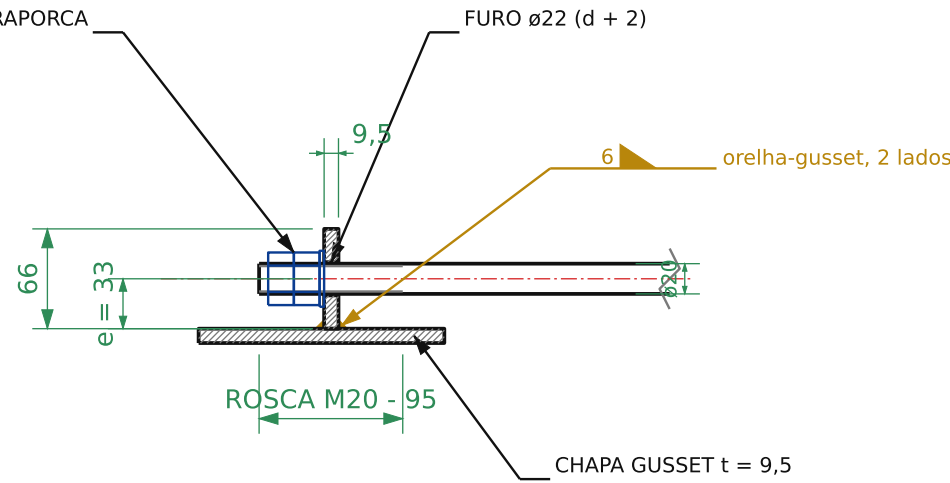

CORTE B-B - PONTA DO TIRANTE
ESCALA 1:5

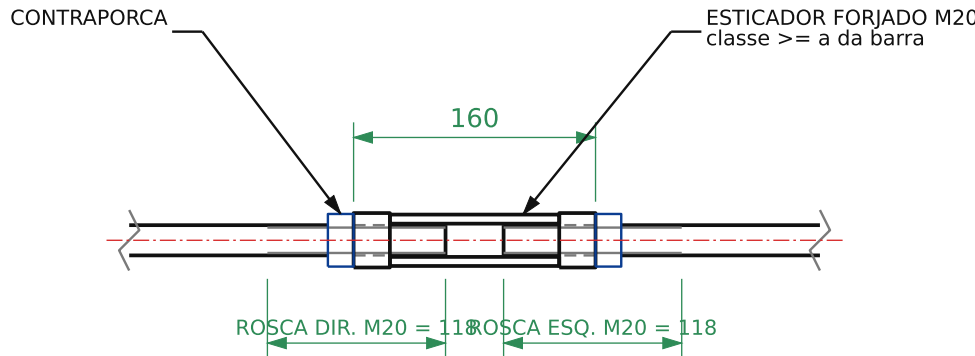

VISTA C - ESTICADOR NO MEIO DA DIAGONAL
ESCALA 1:5

NOTAS

- Cotas em milímetros.
- Tirantes $\varnothing 20$ mm com rosca M20 nas pontas ($A_e = 0,75 A_g$, NBR 8800 item 5.2.8).
- Orelha $t = 9,5$ mm soldada a chapa gusset $t = 9,5$ mm; gusset soldado a mesa, filete 6 mm.
- Furo $\varnothing 22$ na orelha; arruela, porca e contraporca do lado do PT.
- Esticador no meio da diagonal; pre-tracionar apos o prumo.
- Tirantes so trabalham a tracao e nao se ligam no cruzamento.
- Esticador de 160 mm adotado para o desenho; confirmar no catalogo.
- Contraventamento vertical: tirante $\varnothing 20$ mm, mesmas pontas e esticador.
- Escora TC 88,9x3,2 (3") adotada no detalhamento; nao consta do calculo.

NO DE CONTRAVENTAMENTO

ESCALA 1:5

OBRA
Galpao Exemplo
CLIENTE
Cliente Exemplo Ltda

TÍTULO DO DESENHO
Nó de contraventamento
No de contraventamento

RESPONSÁVEL TÉCNICO
Eng. Responsavel Tecnico
CREA nº _____ — ART nº _____

ESCALA
1:5
DATA 11/09/2026

PRANCHA
05/06
REV. 00

Desenho gerado automaticamente. Deve ser conferido e assinado por engenheiro habilitado, com ART no CREA, antes da fabricação.